




Signature Not
Verified
Signed by Assistant Director
Local Body Chennai
Date 2026/09/16 16:25:27

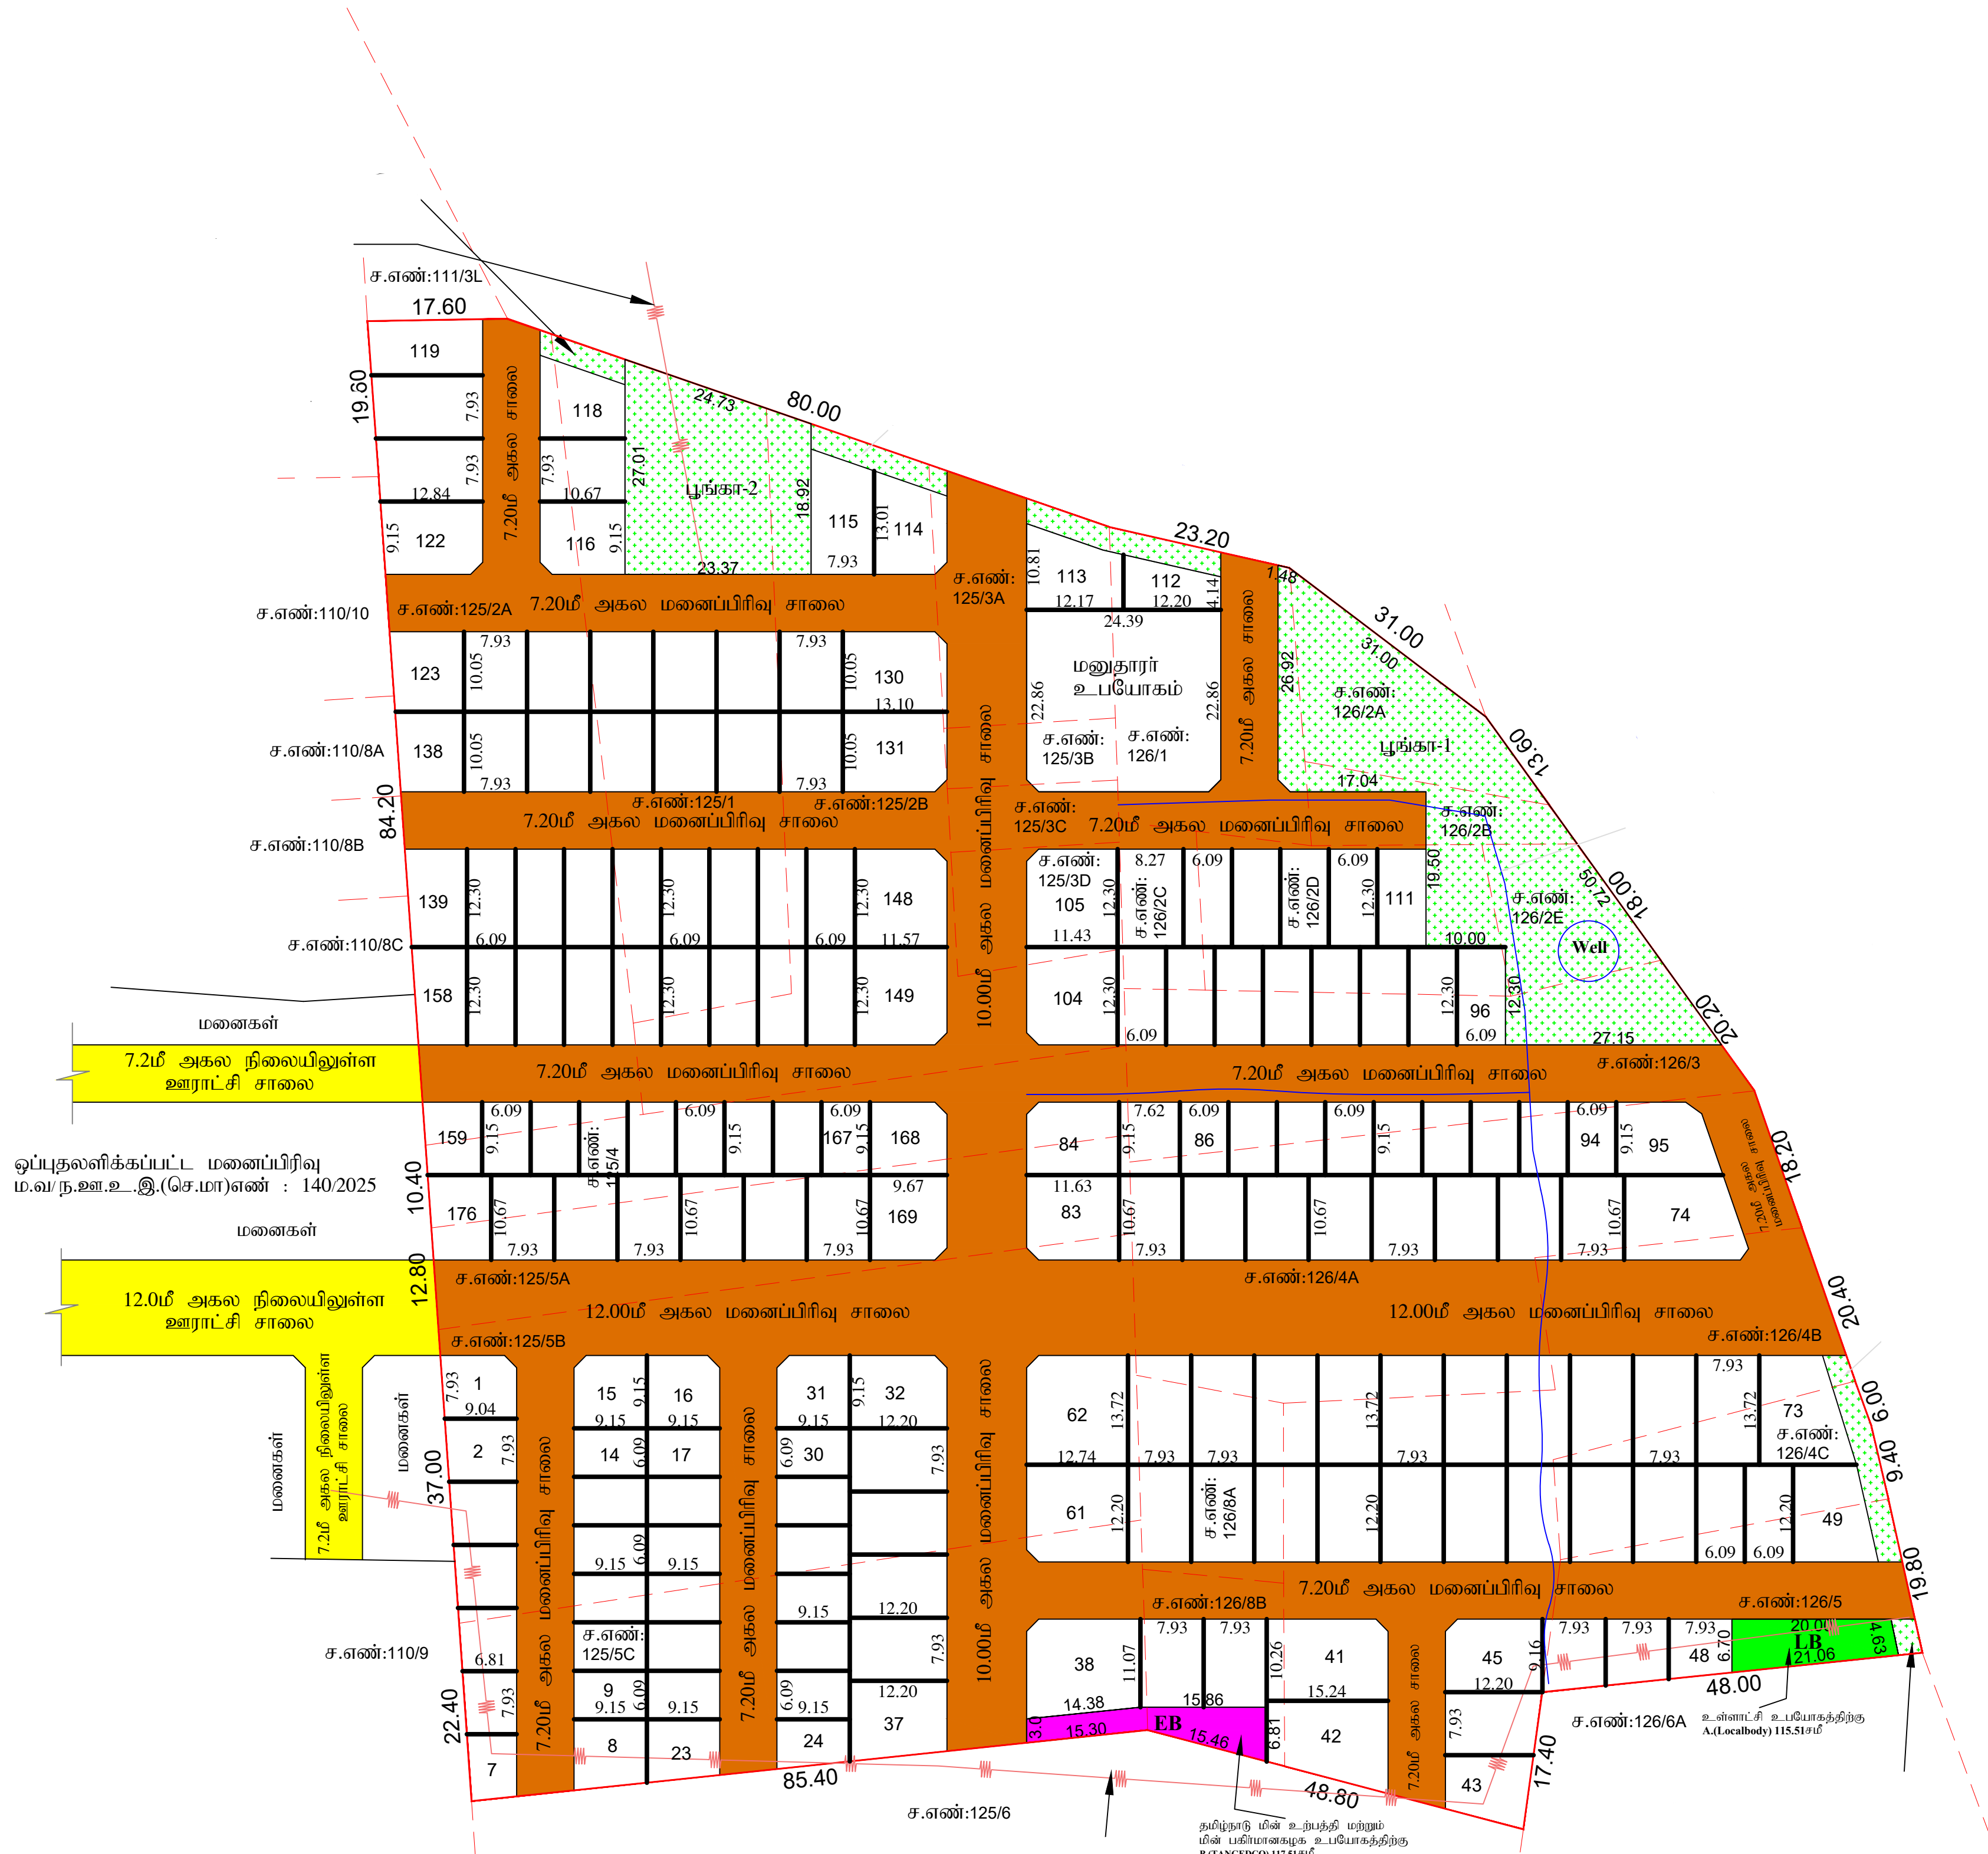

நகர் ஊரமைப்பு துறை	
செங்கல்பட்டு மாவட்ட நகர் ஊரமைப்பு அலுவலகம்	
மதுராந்தகம் ஊராட்சி ஒன்றியம்	
உத்தேச குடியிருப்பு மனைப்பிரிவிற்கான தொழில்நுட்ப ஒப்புதல் வரைபடம்	
மாவட்டம்	: செங்கல்பட்டு
வட்டம்	: மதுராந்தகம்
ஊராட்சி	: பழையனூர் (திட்டமில்லாபகுதி)
கிராமம்	: பழையனூர் (திட்டமில்லாபகுதி)
நில அளவை எண்கள்	: 125/1, 125/2A, 125/2B, 125/3A, 125/3B, 125/3C, 125/3D, 125/4, 125/5A, 125/5B, 125/5C, 126/1, 126/2A, 126/2B, 126/2C, 126/2D, 126/2E, 126/3, 126/4A, 126/4B, 126/4C, 126/5, 126/8A & 126/8B
இணையதள விண்ணப்ப எண்	: PSBC8DHP/2026
அளவு	: 1 : 400
குறிப்பு	
மனைப்பிரிவு இடத்தின் பரப்பு	: 25600 ச.மீ. (6.32 ஏக்கர்)
கோரிய மனைகள்	: 131
ஒதுக்கிய மனைகள்	: 131 + மனுதாரர் உபயோகம்
EWS மனைகள்	: 2-7, 9-14, 17-30, 86-94, 112 & 159-167
EWS மனைகள் பரப்பு	: 2936.25 ச.மீ (10.60%)
மனைப்பிரிவின் எல்லை	:
நிலையிலுள்ள சாலை	:
உத்தேச மனைப்பிரிவு சாலை	:
பொது ஒதுக்கீடு :	
மனைப்பிரிவு இடத்தின் பரப்பு	: 25600.00 ச.மீ. (6.32 ஏக்கர்)
மனைப்பிரிவு சாலையின் பரப்பு	: 8403.90 ச.மீ.
மனைப்பிரிவு சாலையின் பரப்பு போக	
மனைப்பிரிவு இடத்தின் பரப்பு	: 17196.10 ச.மீ.
A.பொது ஒதுக்கீடுகள். (மனுதாரரால் தான பத்திர எண்.6032/2026 நாள்.19.08.2026-ன் மூலம் கீழ்க்கண்டவாறு உள்ளாட்சிக்கு ஒப்படைப்பு செய்யப்பட்டுள்ளது)	
1. . உத்தேச சாலைகள் மற்றும் மூலை முடக்குகளின் பரப்பளவு	: 8403.90 ச.மீ
2. பூங்கா-1	: 1228.90 ச.மீ
3. பூங்கா-2	: 536.75 ச.மீ
பூங்காவின் மொத்த பரப்பளவு	: 1765.65 ச.மீ (10.26%)
B.பொது உபயோகம்: TNCD&BR 2019, 47(8) - ன் படி தானமாக ஒப்படைக்கப்பட்டவை.	
1. உள்ளாட்சிக்கு ஒப்படைக்கப்பட்ட மனைப்பரப்பு	: 115.50 ச.மீ (0.67%)
2. TANGEDCO ஒப்படைக்கப்பட்ட மனைப்பரப்பு	: 117.50 ச.மீ (0.68%)
மூலை முடக்கு	: 7.2மீ முதல் 12.0மீ அகல் சாலைகள் வரை - 1.5மீ x 1.5மீ,
நிபந்தனைகள்.	
1. இம்மனைப்பிரிவுக்கு உள்ளாட்சியால் ஒப்புதலளிக்கும் முன் இடத்தில் எந்தத் துறையாலும் நில ஆர்ஜித நடவடிக்கை எடுக்கப்படவில்லை என்றும், நில ஆர்ஜிதம் செய்து தரக்கேரீ மாவட்ட வருவாய் அலுவலரிடமிருந்து உத்தேசங்கள் ஏதும் பெறப்படவில்லை என்றும் உள்ளாட்சி நிர்வாக அதிகாரி உறுதி செய்துகொள்ள வேண்டும்.	
2. அரசாணை எண்.18 நகராட்சி நிர்வாகம் மற்றும் குடிநீர் வழங்கல் துறை, நாள்.04.02.2019 மற்றும் அரசாணை எண்.16 நகராட்சி நிர்வாகம் மற்றும் குடிநீர் வழங்கல் துறை, நாள்.31.01.2020-ன்படி சாலை ஒதுக்கீடுகள் மற்றும் பொது உபயோக பகுதியினை உள்ளாட்சியே தானமாக பெற்றுக்கொண்டு பராமரிக்க வேண்டும் என்றும் நில உரிமம் குறித்து உள்ளாட்சியே முழு பொறுப்பு என்றும் தெரிவிக்கப்படுகிறது.	
3. இம்மனைப்பிரிவுக்கு உள்ளாட்சியால் ஒப்புதலளிக்கும் முன் அரசாணை எண்.181 விட்டு வசதி (ம) நகர்ப்புற வளர்ச்சி நவ.4(1) துறை, நாள்.09.12.2020 - ல் குறிப்பிட்டுள்ள கீழ்க்கண்ட வழிகாட்டுதல்களை தவிராமல் பின்பற்றப்பட வேண்டும்.	
" The local body would grant final approval / License to the layout and would release the final layout drawings to the applicant only after ensuring that the applicant lays tar roads, provide other amenities like storm water drains, water supply facilities by constructing required OHT, provide necessary street lights etc., as per the standards specified by the local body. Further, the local body should intimate the fact of release of final layout drawing and the details of the amenities provided for the layout to the planning authority."	
4. நில உரிமம் குறித்து சமர்ப்பிக்கப்பட்ட சான்றுகள் மற்றும் பரிசீலனைக்குச் சமர்ப்பிக்கப்பட்ட ஆவணங்கள் சரியானவை அல்ல என அறியப்பட்டால் அல்லது மனைப்பிரிவுக்குத் தொழில்நுட்ப ஒப்புதல் வழங்கியதால் பாதிப்பு ஏற்படக்கூடிய சூழ்நிலை ஏற்படின், மனைப்பிரிவுக்கு வழங்கப்பட்ட தொழில்நுட்ப ஒப்புதல் எவ்வித முன்னறிவிப்புமின்றி நகர் ஊரமைப்பு இயக்குநர், சென்னை அவர்களால் இரத்து செய்யப்படும்.	
5. இவ்வலுவலகத்தால் தொழில் நுட்ப ஒப்புதல் அளிக்கப்படும் மனைப்பிரிவு மனைகள் வாங்கும் ஒவ்வொரு மனுதாரருக்கும் ஒப்புதலளிக்கப்பட்ட மனைப்பிரிவு வரைபட நகல் வழங்கப்பட வேண்டும்.	
6. இவ்வலுவலகத்தால் தொழில் நுட்ப ஒப்புதல் அளிக்கப்படும் மனைப்பிரிவு வரைபடத்தினை பொதுமக்கள் பார்வைக்காக சம்பந்தப்பட்ட இடத்தில் 6'x4' என்ற அளவுக்குக் குறையாமல் கான்கிரீட் பலகையில் வரைந்து வைக்கப்பட வேண்டும்.	
7. மனைப்பிரிவின் ஊடே செல்லும் நிறிலைகளை தடைசெய்யாமல் நிலைநிறுத்தப்பட வேண்டும்.	
8. நிறிலைகள் பாதிக்கப்படாத வண்ணம் கட்டடம் கட்டப்படவேண்டும்.	
9. இம்மனைப்பிரிவிலிருந்து அருகிலுள்ள இடத்திற்கு செல்லும் வரைபடத்தில் கான்கிரீட் செய்யப்பட்டுள்ளவாறு மனைப்பிரிவின் சாலைகளின் குறுக்கே சாலையின் போக்கினை பாதிக்கும் வகையில் கற்றுக்கால் கட்டப்பட்டிருப்பின் அகற்றப்படும் வேண்டும்.	
10. உத்தேச மனைப்பிரிவு சாலைகளுக்கு மனுதாரரால் தார் சாலை அமைக்கப்பட்டு (BDO / UE) வட்டார வளர்ச்சி அலுவலர் / பொறியாளர் அவர்களிடம் தரம் குறித்து தகுதிச்சான்று பெறப்பட்ட பின்னர் உள்ளாட்சியால் இறுதி ஒப்புதல் வழங்கப்பட வேண்டும்.	
சிறப்பு நிபந்தனைகள்.	
நகர் ஊரமைப்பு துறை சட்டபூர்வமாக தொழில்நுட்ப அனுமதி அளிப்பதன் மூலம் விண்ணப்பதாரரின் பெயரிலுள்ள உரிமையை உறுதிப்படுத்தவில்லை தொழில்நுட்ப அனுமதி / திட்ட அனுமதி அளிப்பதற்கு முன்பு விண்ணப்பதாரரின் விண்ணப்பத்துடன் சமர்ப்பித்த ஆவணங்களில் (கிரைய பத்திரம், பொது அதிகார பத்திரம், குத்தகை பத்திரம், தானபத்திரம், பட்டா மேலும் பல விண்ணப்பதாரர் வளர்ச்சி செய்ய உரிமை உள்ளதா என்று பார்க்கப்படுகிறது.	
சொத்தினை வாங்க விரும்பும் எந்த நபரும் விண்ணப்பதாரருக்கு சொத்தின்மீது உள்ள உரிமையை தவிராக உறுதிப்படுத்தி கொள்ள வேண்டும். மேலும் அதன் மேல் தனி நபர் உரிமை கோரினால் அவர்கள் அதனை பொறுத்தமாத் தகுதியுள்ள நீதிமன்றத்தின் முன் தீர்த்துக்கொள்ளலாம். இதனை முடிவு செய்ய நகர் ஊரமைப்பு துறை பொறுத்தமாத் அமைப்பு அல்ல.	
இம்மனைப்பிரிவு தொடர்பாக நீதிமன்றத்தில் ஏதேனும் ஆணை பெறப்படும் பட்சத்தில் அவ்வாணையின்படி நடவடிக்கை மேற்கொள்ளப்படும்.	
ம.வ/ந.ஊ.உ.இ.(செ.மா) எண் : 246/2026	
உதவி இயக்குநர், மாவட்ட நகர் ஊரமைப்பு அலுவலகம், செங்கல்பட்டு மாவட்டம்	